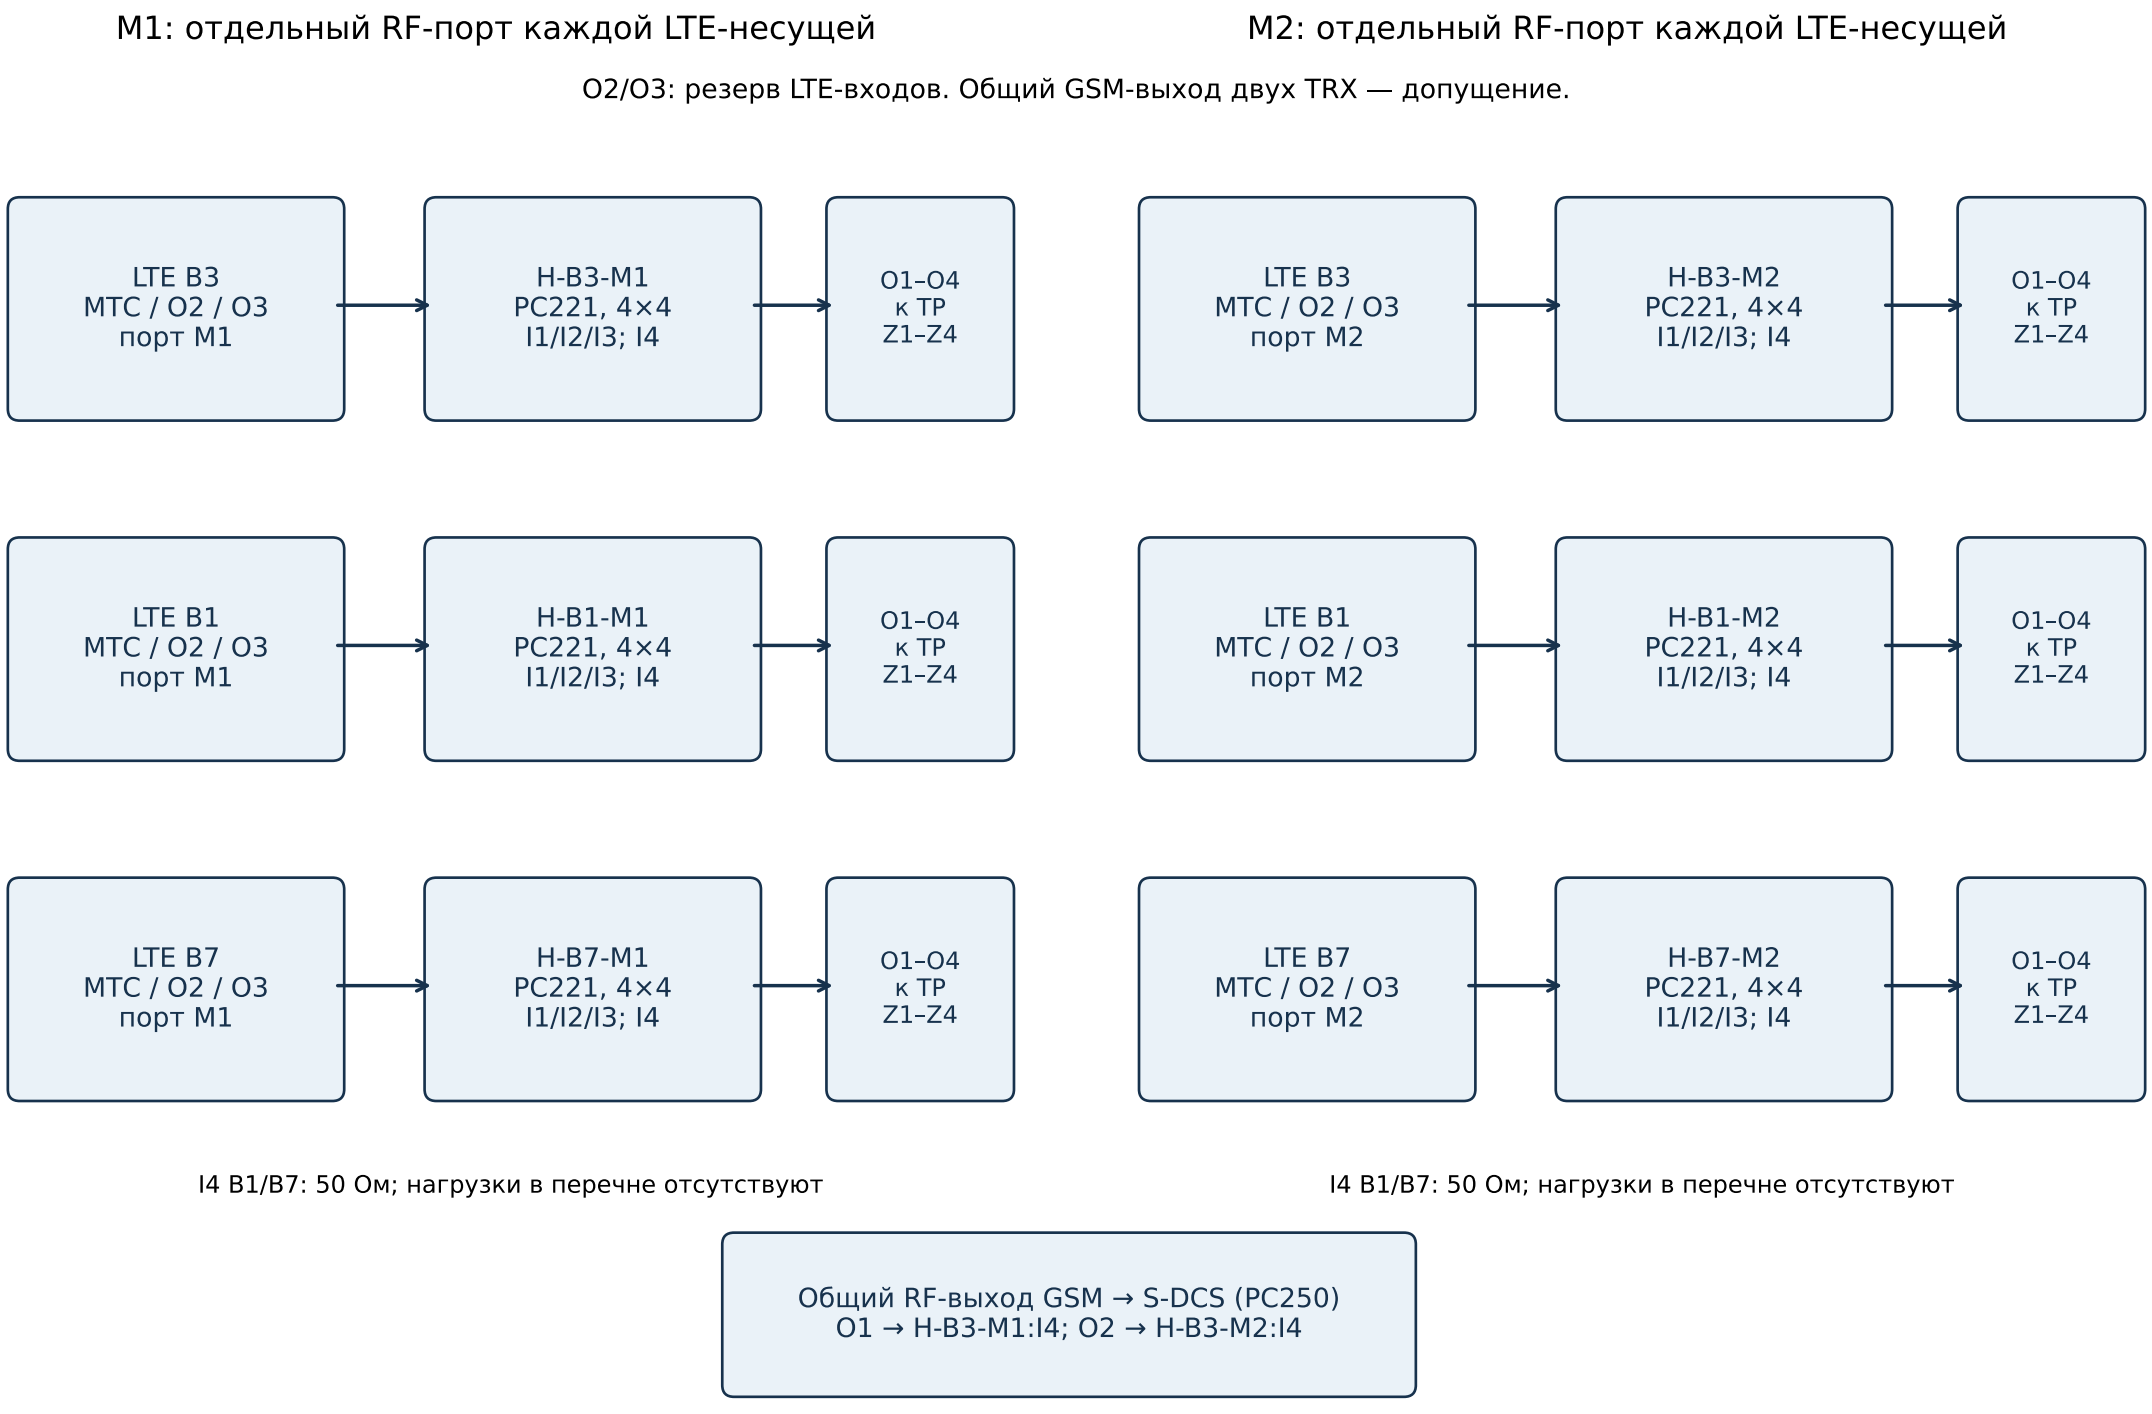Подключение БС к головному узлу: две независимые MIMO-ветви