
Первый этаж: один LTE-пул B3/B1/B7; 32 In06
S — PC250; Q — PC252; M1/M2 отдельно, показаны на одной трассе

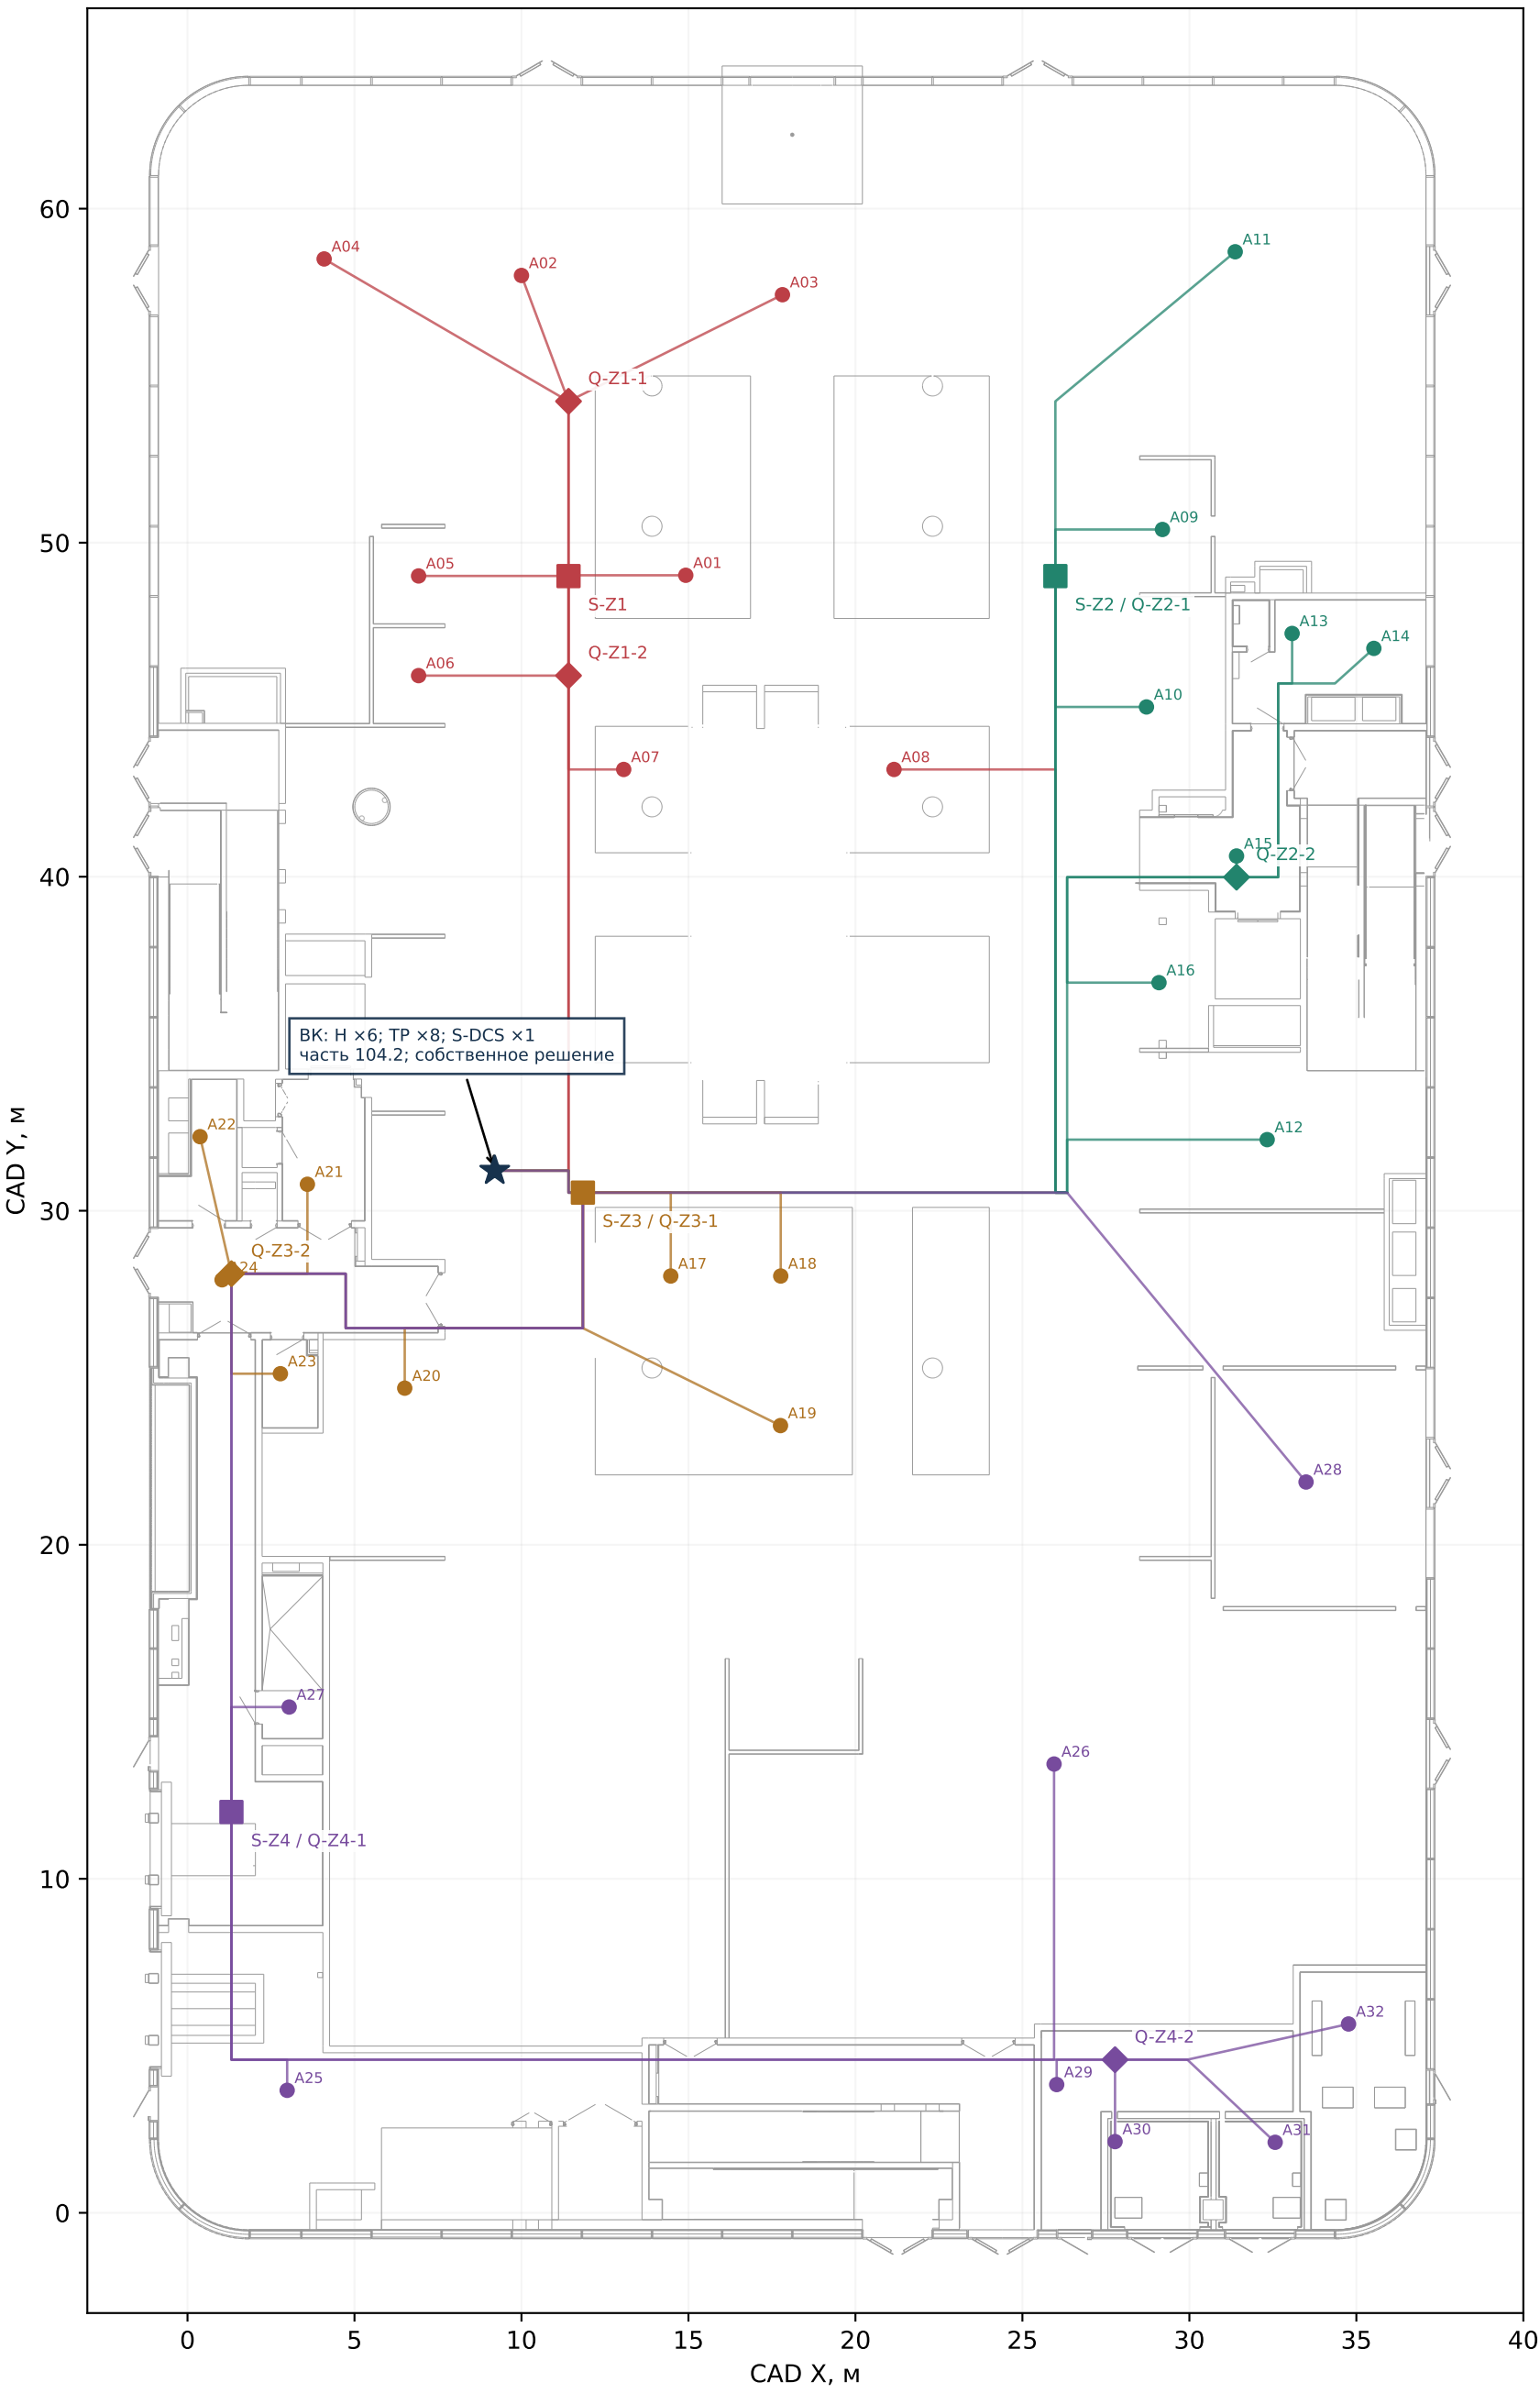

S/Q: по два устройства, M1 и M2. Точные размеры и монтажная раскладка не заданы.
● In06; ■ зональный PC250; ◆ PC252; ★ головной узел. Проектные координаты, не натурная съёмка.