
Первый этаж: один LTE-пул B3/B1/B7; 32 In06
S — PC252; Q1 — PC250; Q2 — PC252; M1/M2 отдельно

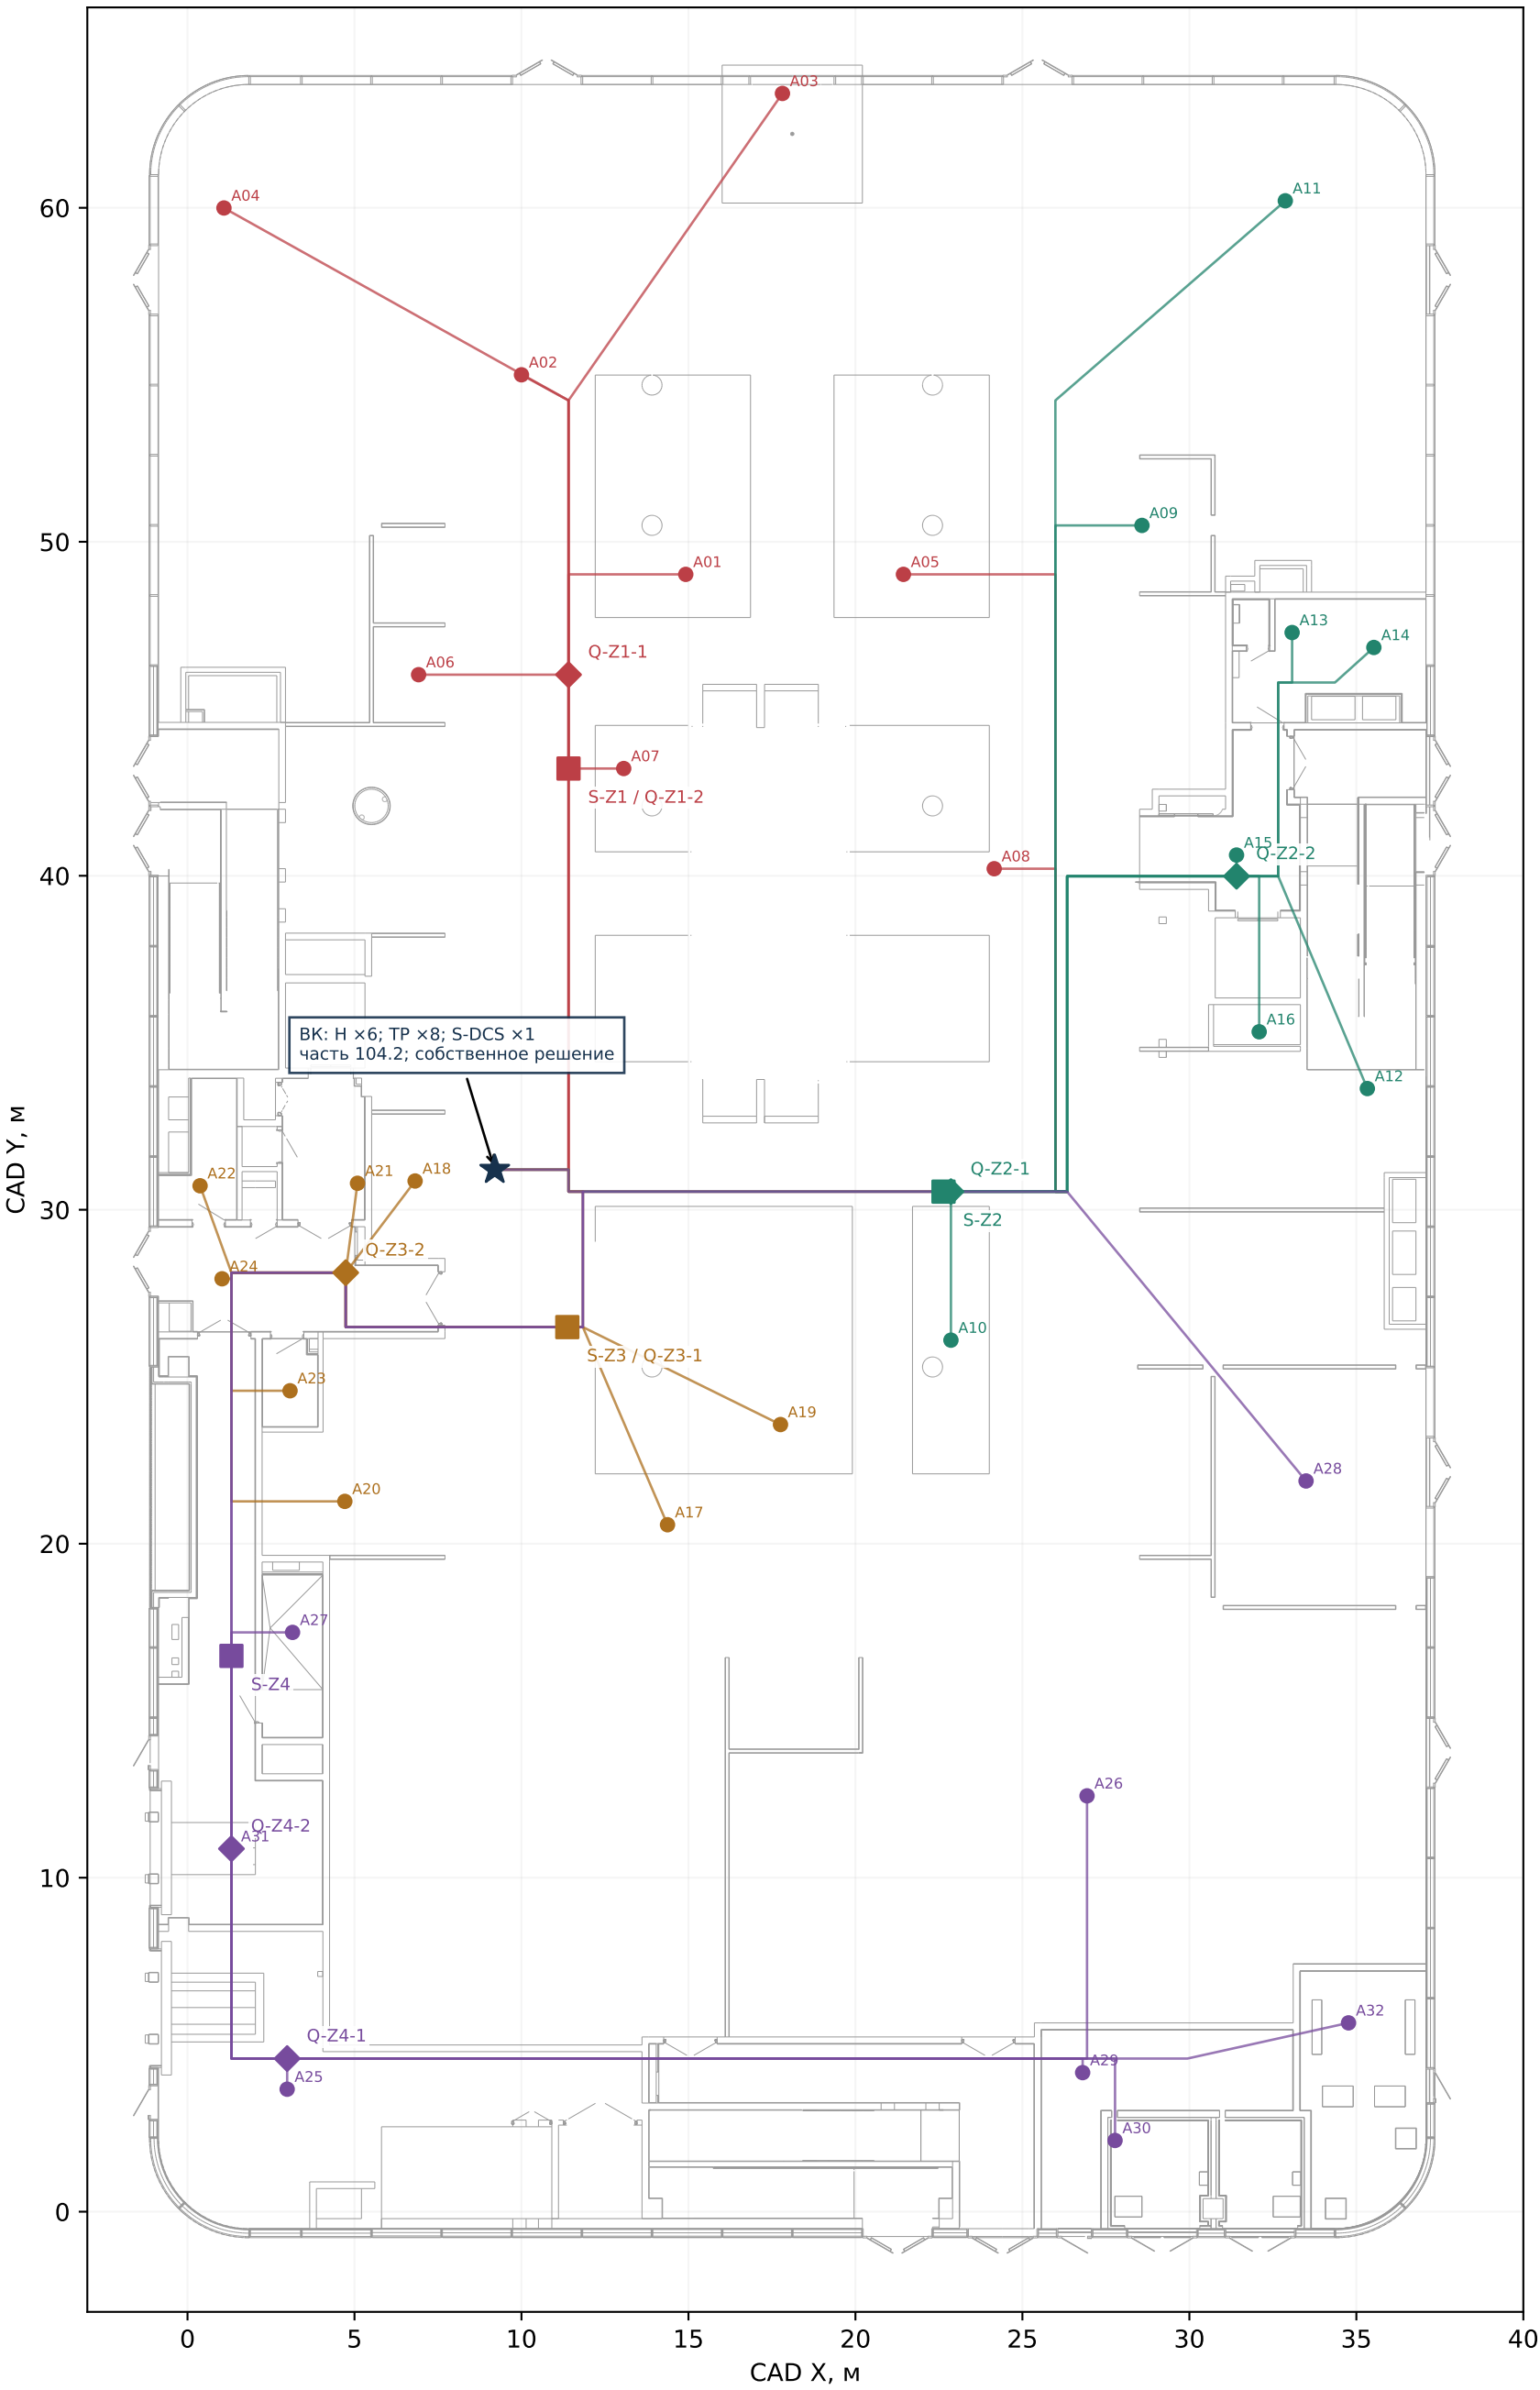

S/Q: по два устройства, M1 и M2. Точные размеры и монтажная раскладка не заданы.
● In06; ■ зональный делитель; ◆ делитель подгруппы; ★ головной узел. Проектные координаты, не натурная съёмка.